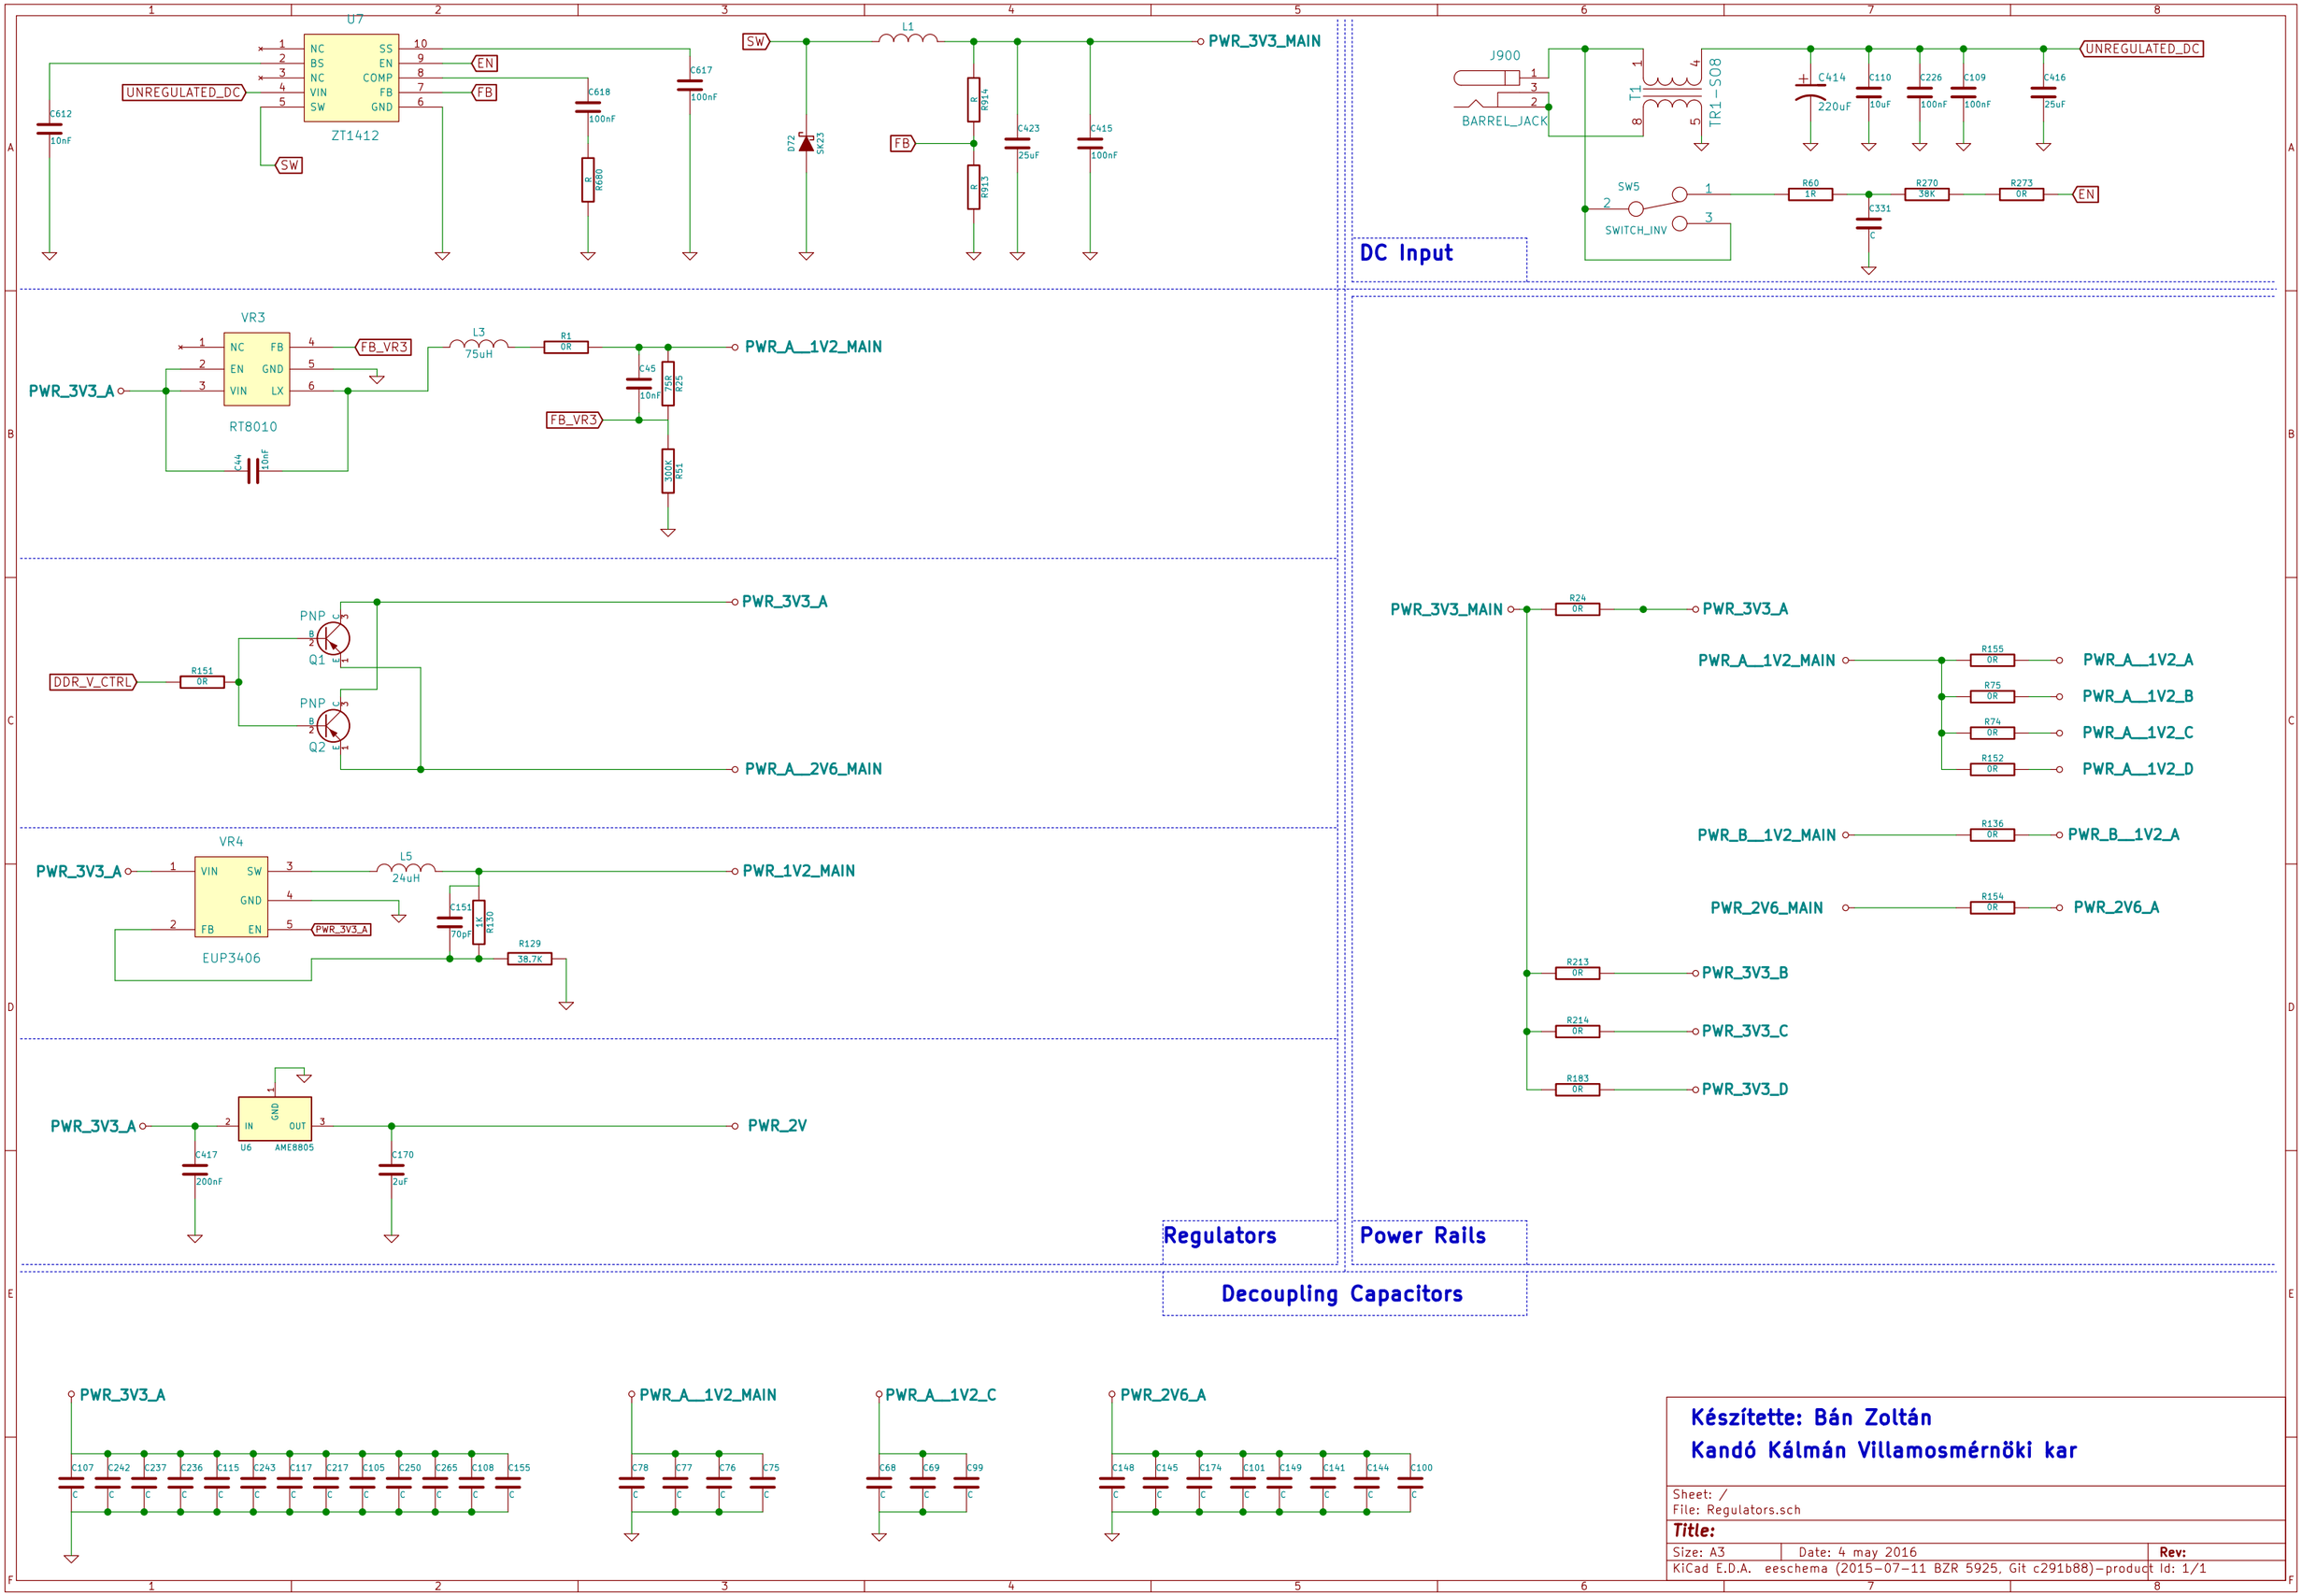

Készítette: Bán Zoltán
Kandó Kálmán Villamosmérnöki kar

Sheet: /
File: Regulators.sch

Title:

Size: A3 | Date: 4 may 2016 | Rev:

KiCad E.D.A. eeschema (2015-07-11 BZR 5925, Git c291b88)-product Id: 1/1